


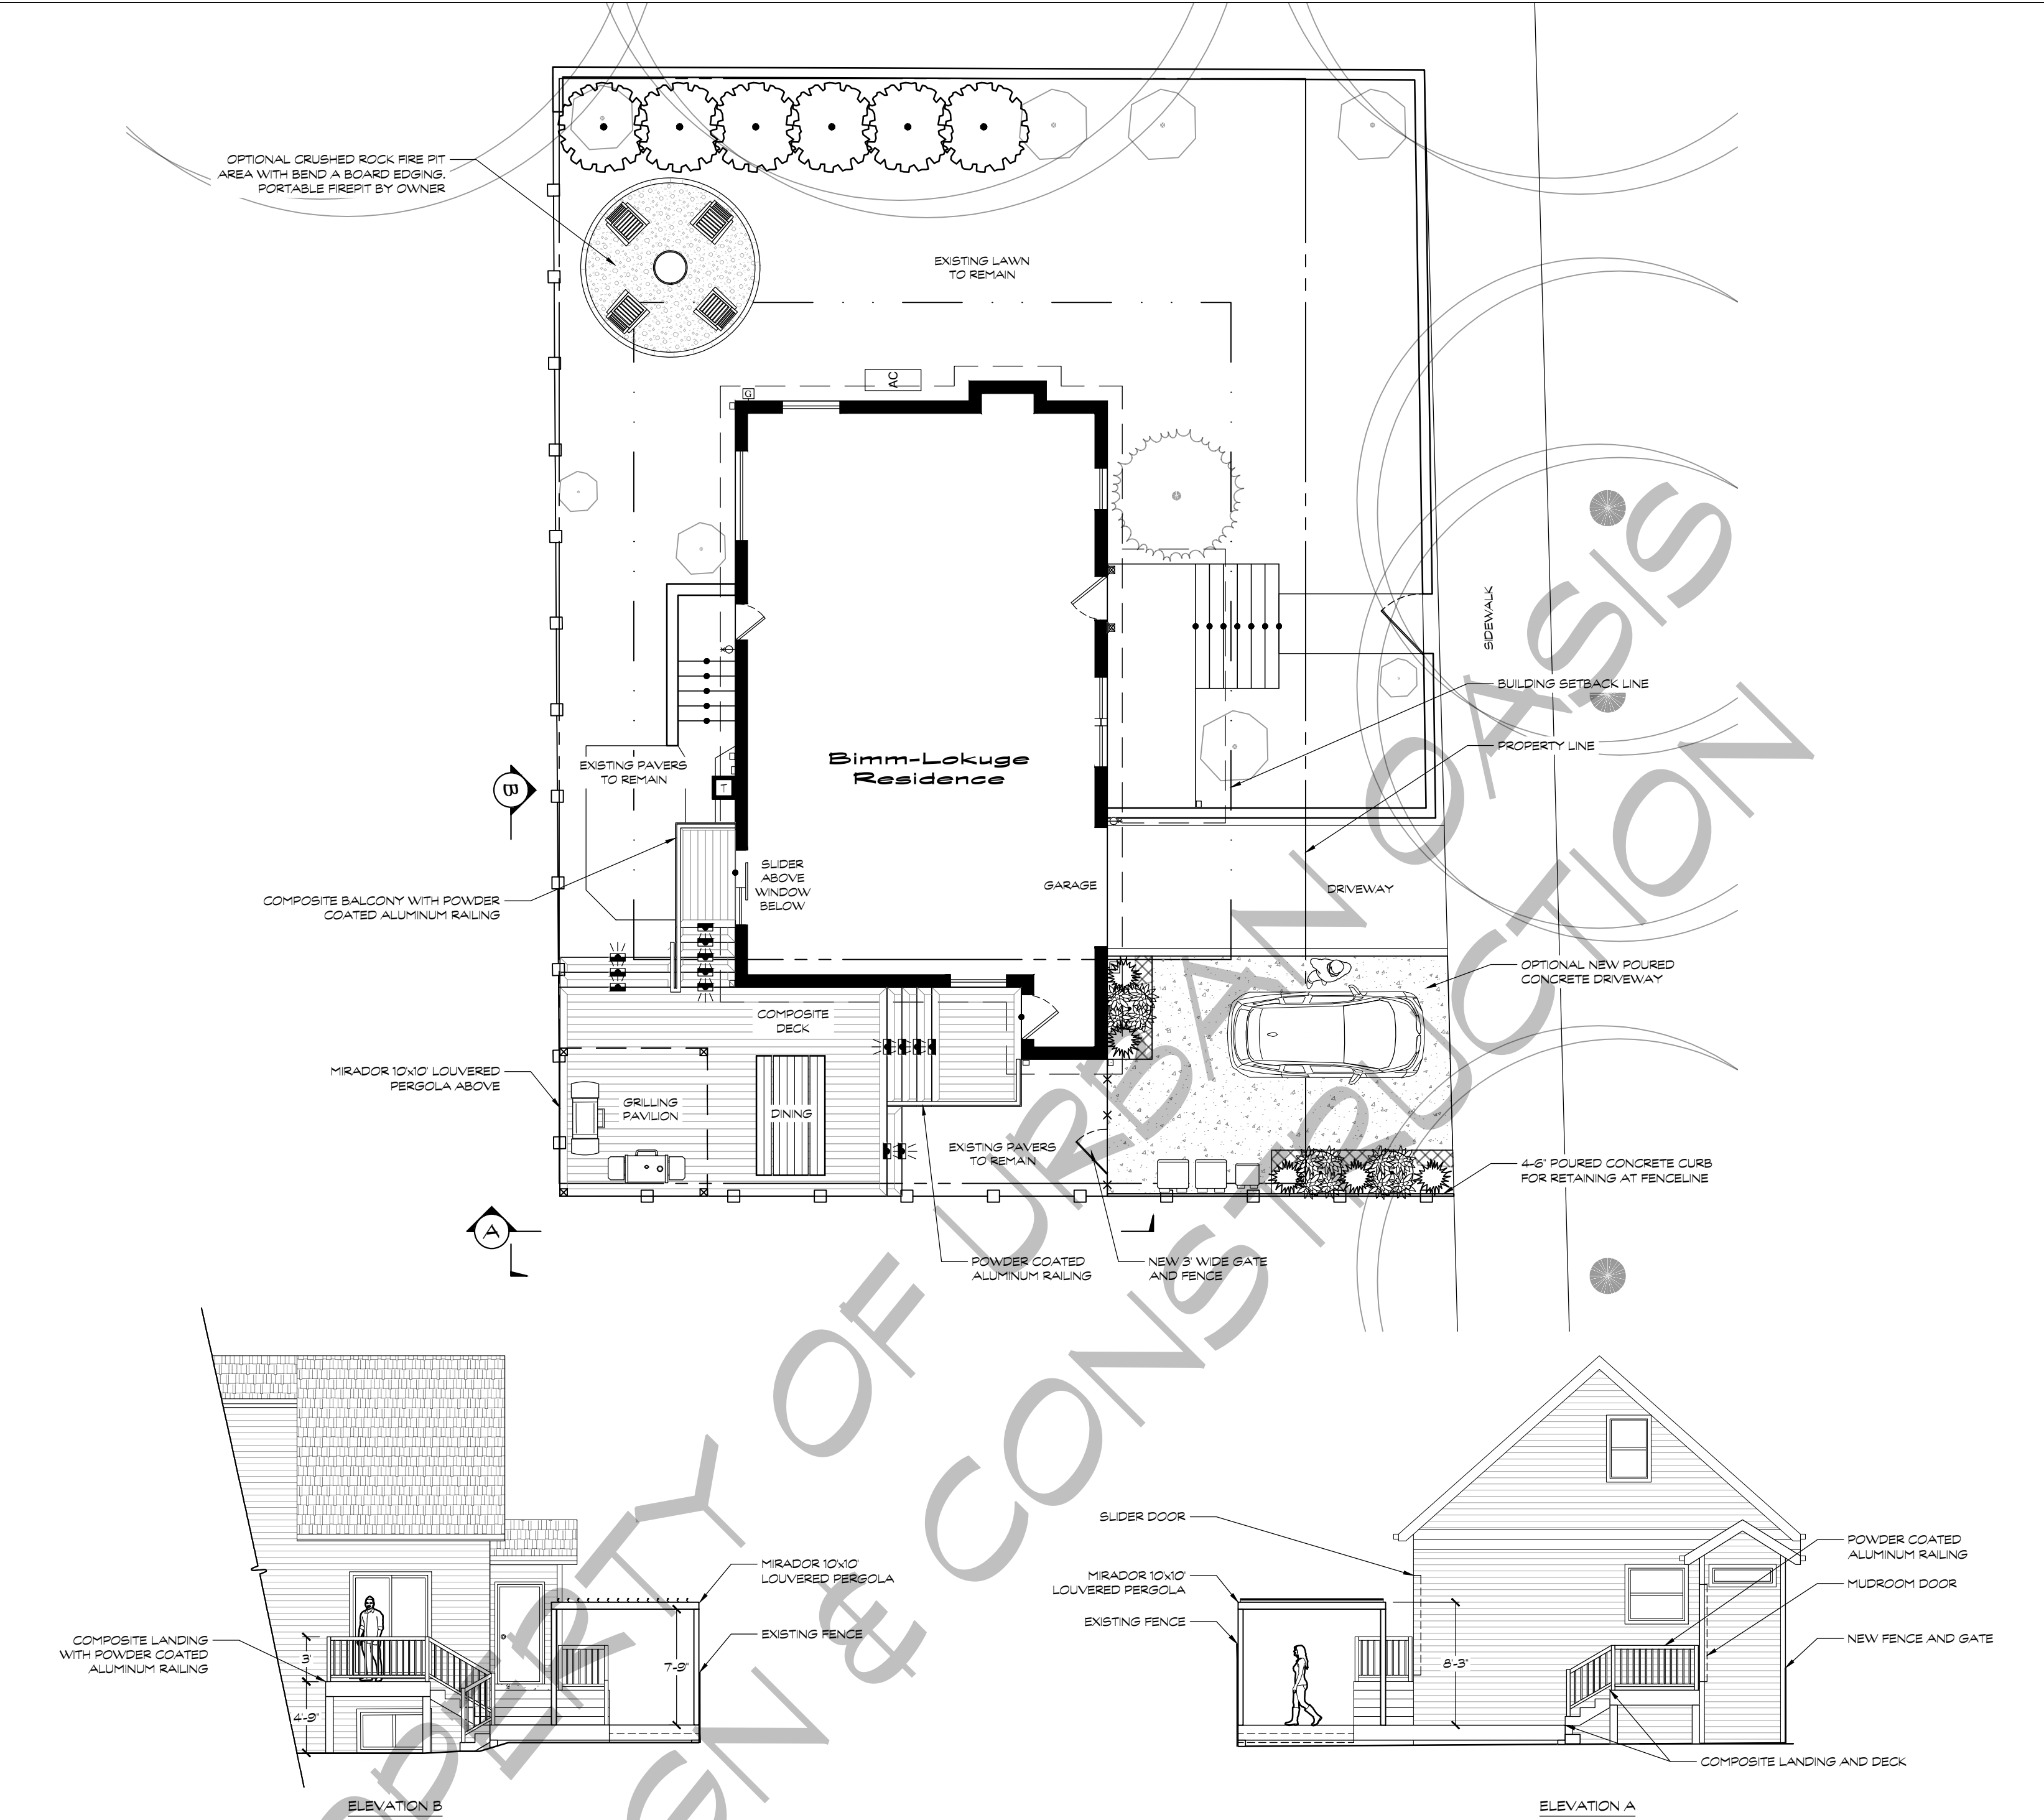


PLANTING SCHEDULE

SYMBOL	BOTANICAL / COMMON NAME	QTY	SIZE
TREES			
	HYDRANGEA PANICULATA 'LITTLE LIME STD' / LITTLE LIME PANICLE HYDRANGEA TREE	3	10 GAL.
SHRUBS			
	PITTOSPORUM TENUIFOLIUM 'SILVER SHEEN' / SILVER SHEEN TAWHIWHI	6	5 GAL.
GRASSES			
	CENCHRUS ALOPECUROIDES 'HAMELN' / HAMELN FOUNTAIN GRASS	5	3 GAL.
PERENNIALS			
	EPIMEDIUM X RUBRUM / RED BARRENWORT	12	1 GAL.
GROUND COVERS			
	SEDUM SPECTABILE 'DRAGON'S BLOOD' / SHOWY STONECROP	1 FLAT	

LIGHTING SCHEDULE

SYMBOL	MANUFACTURER/MODEL/DESCRIPTION	QTY
	FX LUMINAIRE DX TRANSFORMER	1
	STEP LIGHT FX LUMINAIRE LD-LED20W BRASS, (BZ) BRONZE LAMP: LD-ILED, 2W / 2.4VA, 2700K, BEAMSPREAD: VERY WIDE FLOOD	14

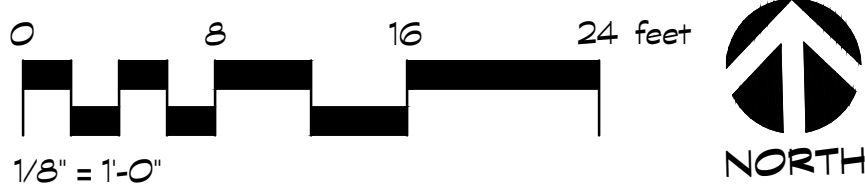

 Urban Oasis Design & Construction LLC
7511 Greenwood Avenue North, #1680
Seattle, Washington 98103

Bimm-Lokuge Residence
2581 6th Ave W
Seattle, WA 98119

Date: 2-23-2026
Plan Title: CONCEPT REVISION

This landscape design is conceptual only. All dimensions are approximate and must be field verified, which may require changes as a result. Plants are subject to change due to availability, size or other factors. This drawing is the exclusive property of Urban Oasis Design & Construction LLC. It may not be used, relied upon by third-parties, or re-produced or distributed to others without our prior written consent.